


## 1-р өдөрхүүн өдүүгүүлэлт

M 1 : 100



## Материалын тэмдэглэсээ

M 1 : 100

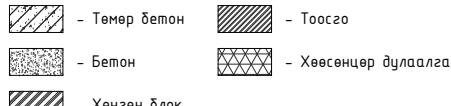

Ταῦλος

1. Үз барылга нь одоо дайгаа газар дээрхүү ногдоон дайгүүламжийн хэмжээг багасгахгүйзэр 1-р дэвхүртн түвшинд дарилгажилт хийхгүйзэр тооцсон бол
  2. Огтолт-1,2,3 – ийн БА-11-13-д үзэн.
  3. Хана болон шалын тодорхойлолтын хувдас БА-34-д үзэн.
  4. Шат-1-ийн хэсэгчилсан дайгүүлэлтийн хувдас БА-24-д үзэн.
  5. Гадна дөвжкоо-1, 2-ийн хэсэгчилсан дайгүүлэлтийн БА-28-д үзэн.

ЗӨВШӨӨРӨЛЦӨН

ББ	Ө.Энхмэнд-од	
ХАС	Б.Нансалмаа	
ЦБЧ	П.Халиуннаа	
ХТ, ДГ	М.Оргил	
ХД	Э.Басанчолам	




Үллаанбаатар хот, Сүхбаатар дүүрэг, 01-р хороо


"ТАНЫ ТӨЛӨӨ БИД" ХХК-ИЙН 6 ДАВХАР ЭМНЭЛГИЙН БАРИЛГЫН ӨРГӨТГӨЛ

1-р дэвхүрүн байгуулалт      № шам: А3

Исполнитель: Э.Анхбаяр  
ЛГ шифр: ПА-02/21  
Паспорт: 1 : 100  
ОГНБ: 9/9/2021 8:42:26 PM

ЦЭМСЭСН	Г.Үүрцааих	ТГ шифр:	Зүргүйн дугаар:	Бүх дугаар:
ДАВЧИН	ДАВЧИН	14Д 11 /21	51-02	51-02

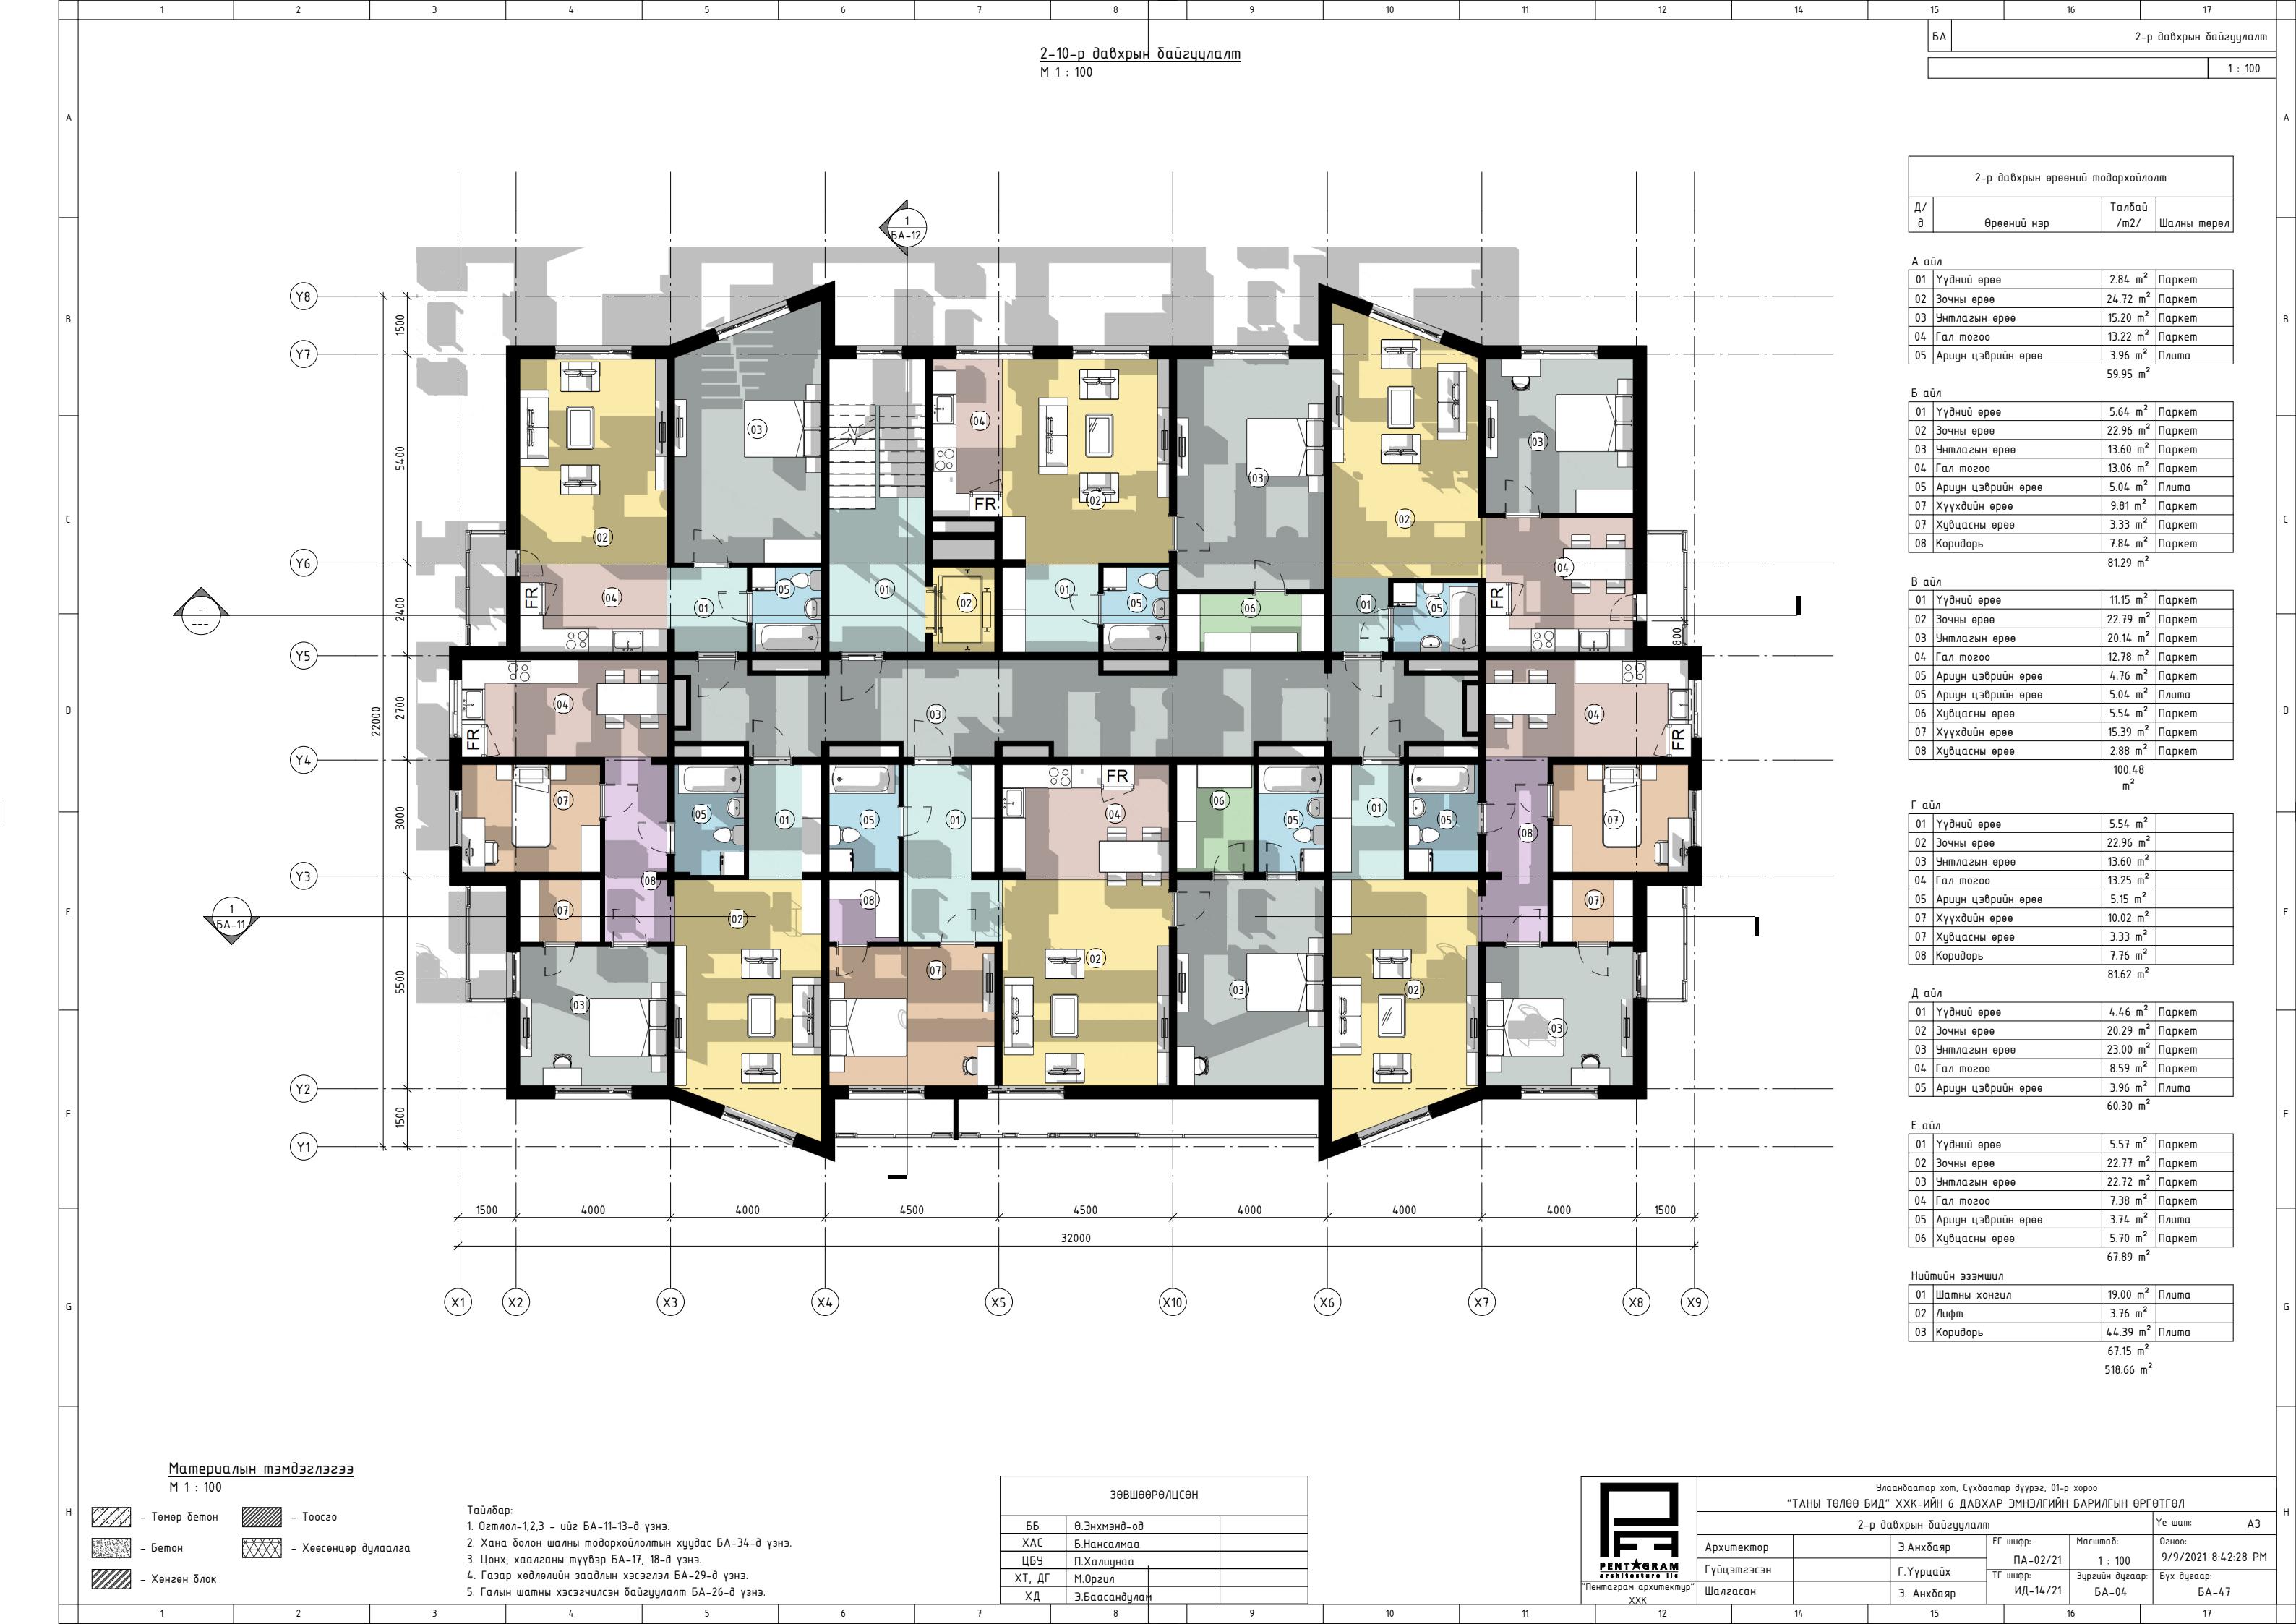

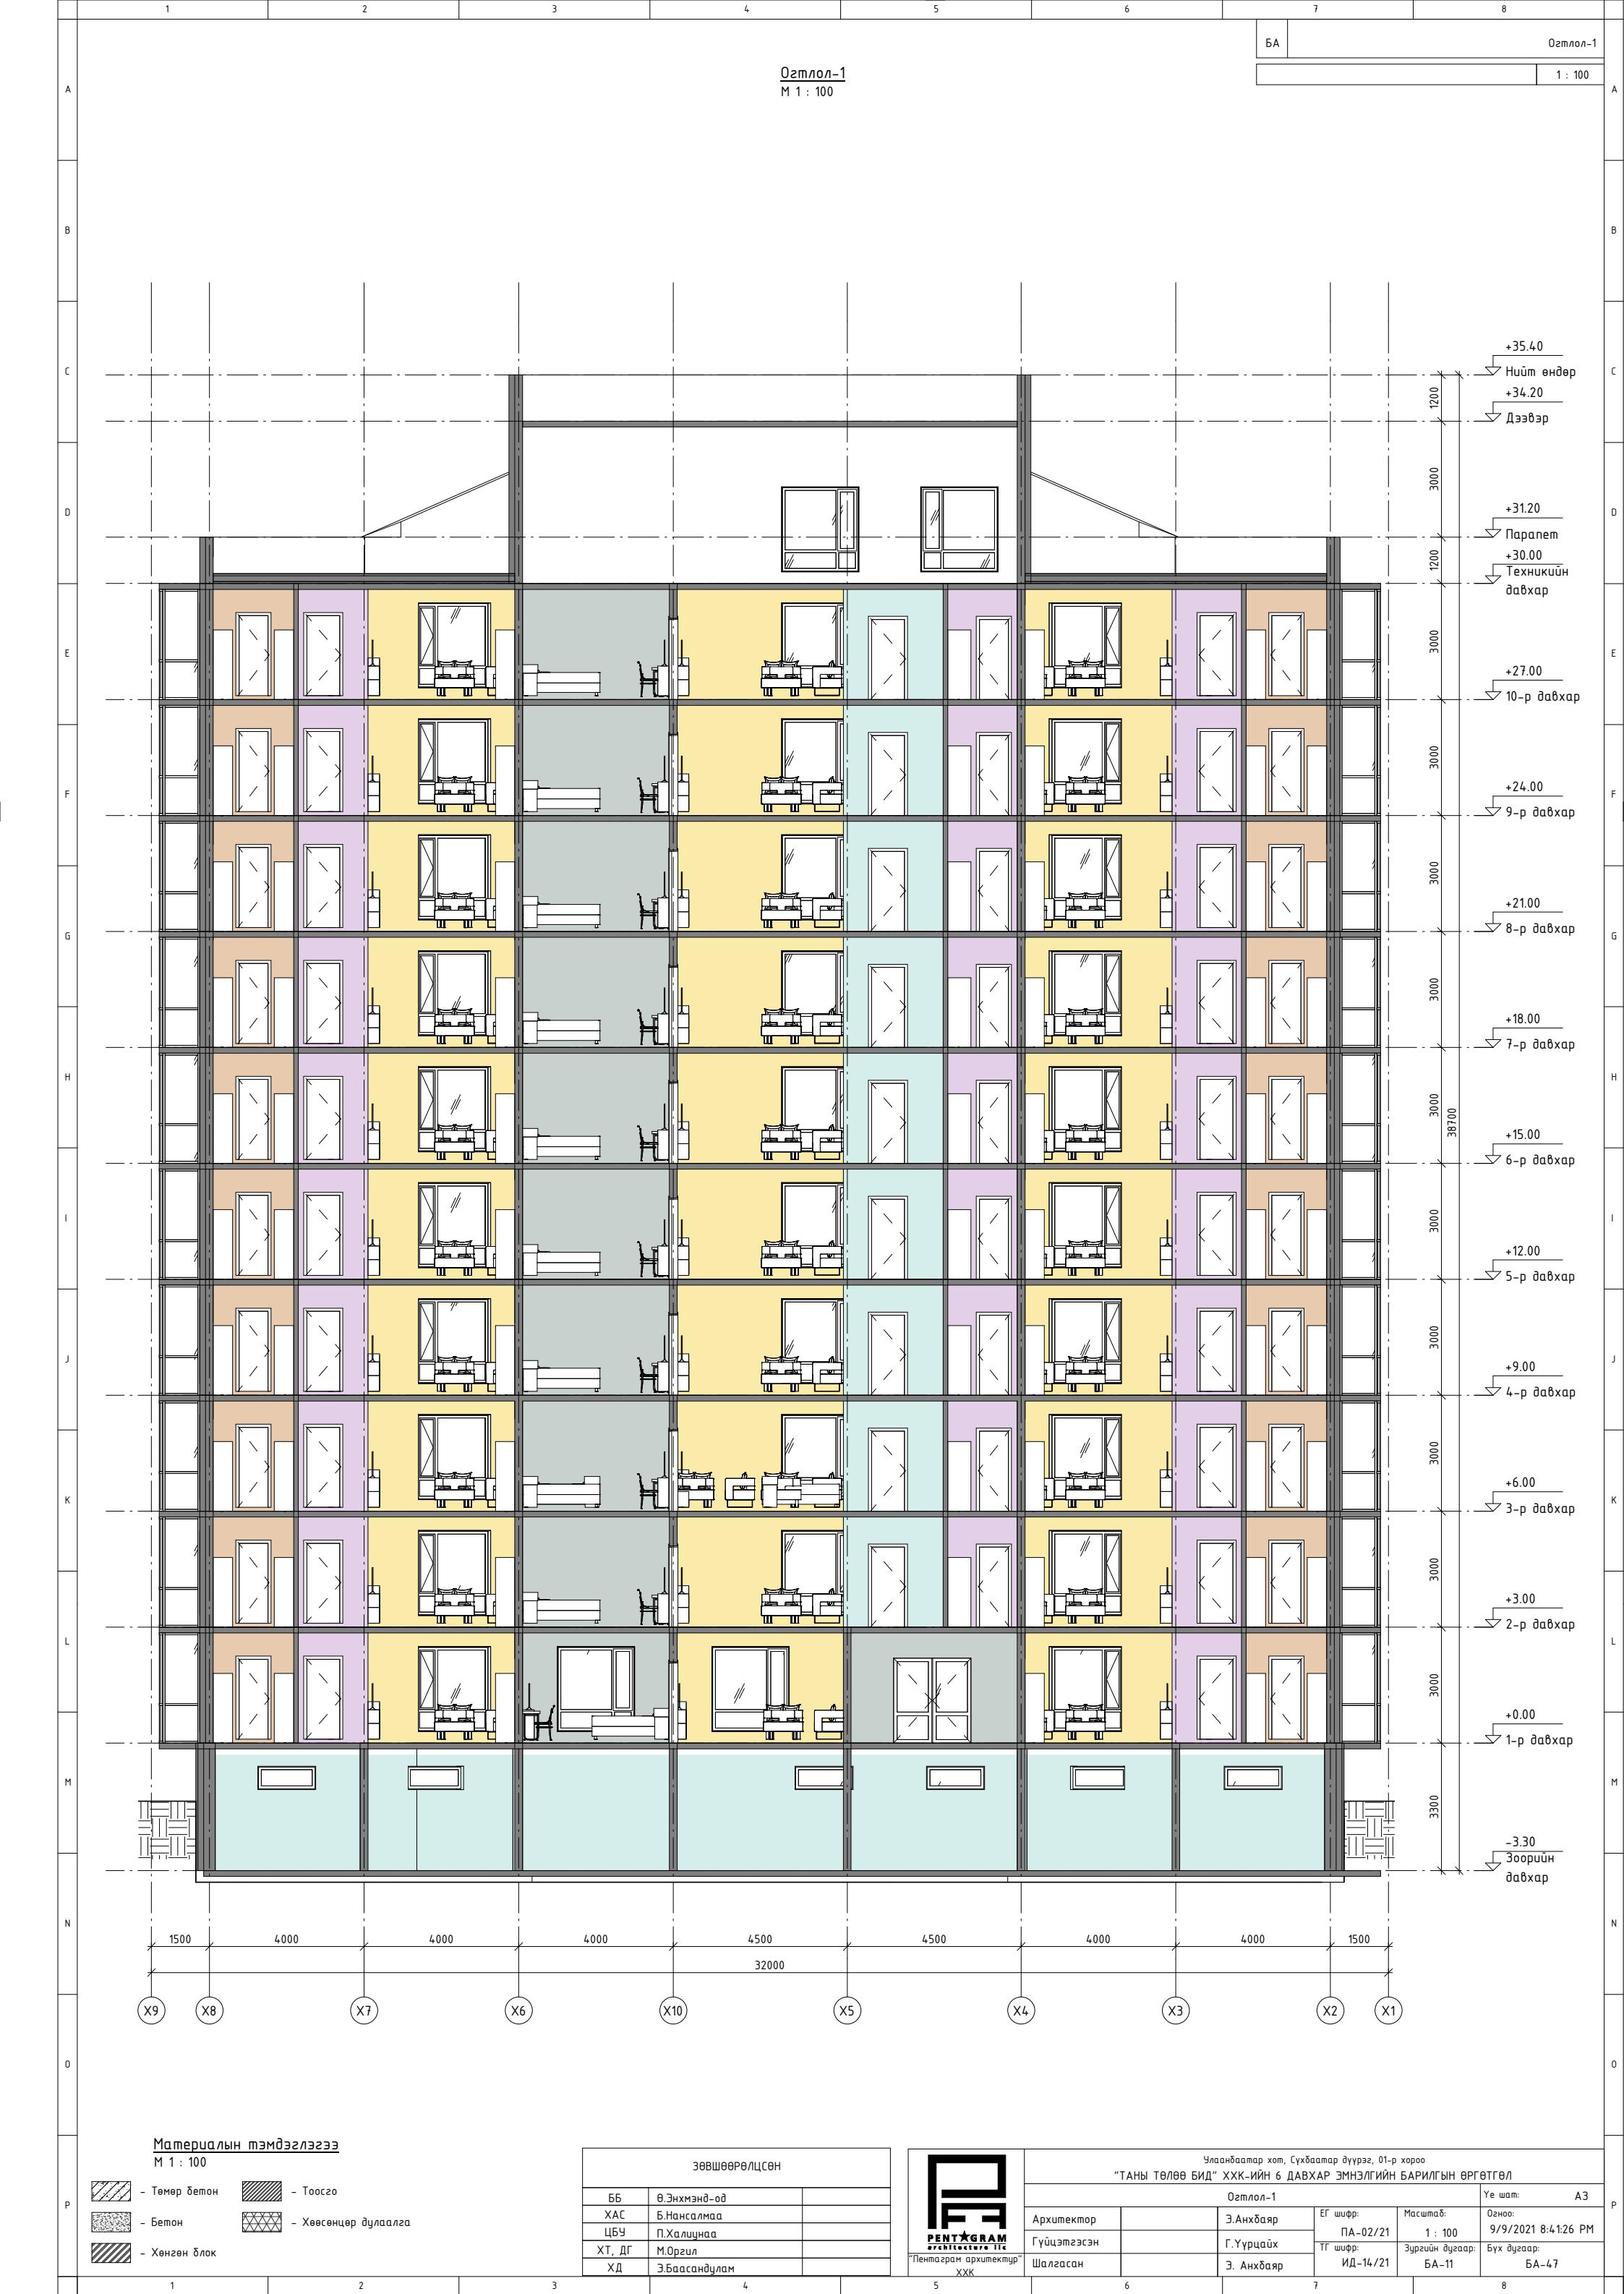


## Огтпол-2

М 1 : 100

БА

Огтпол-2

1 : 100

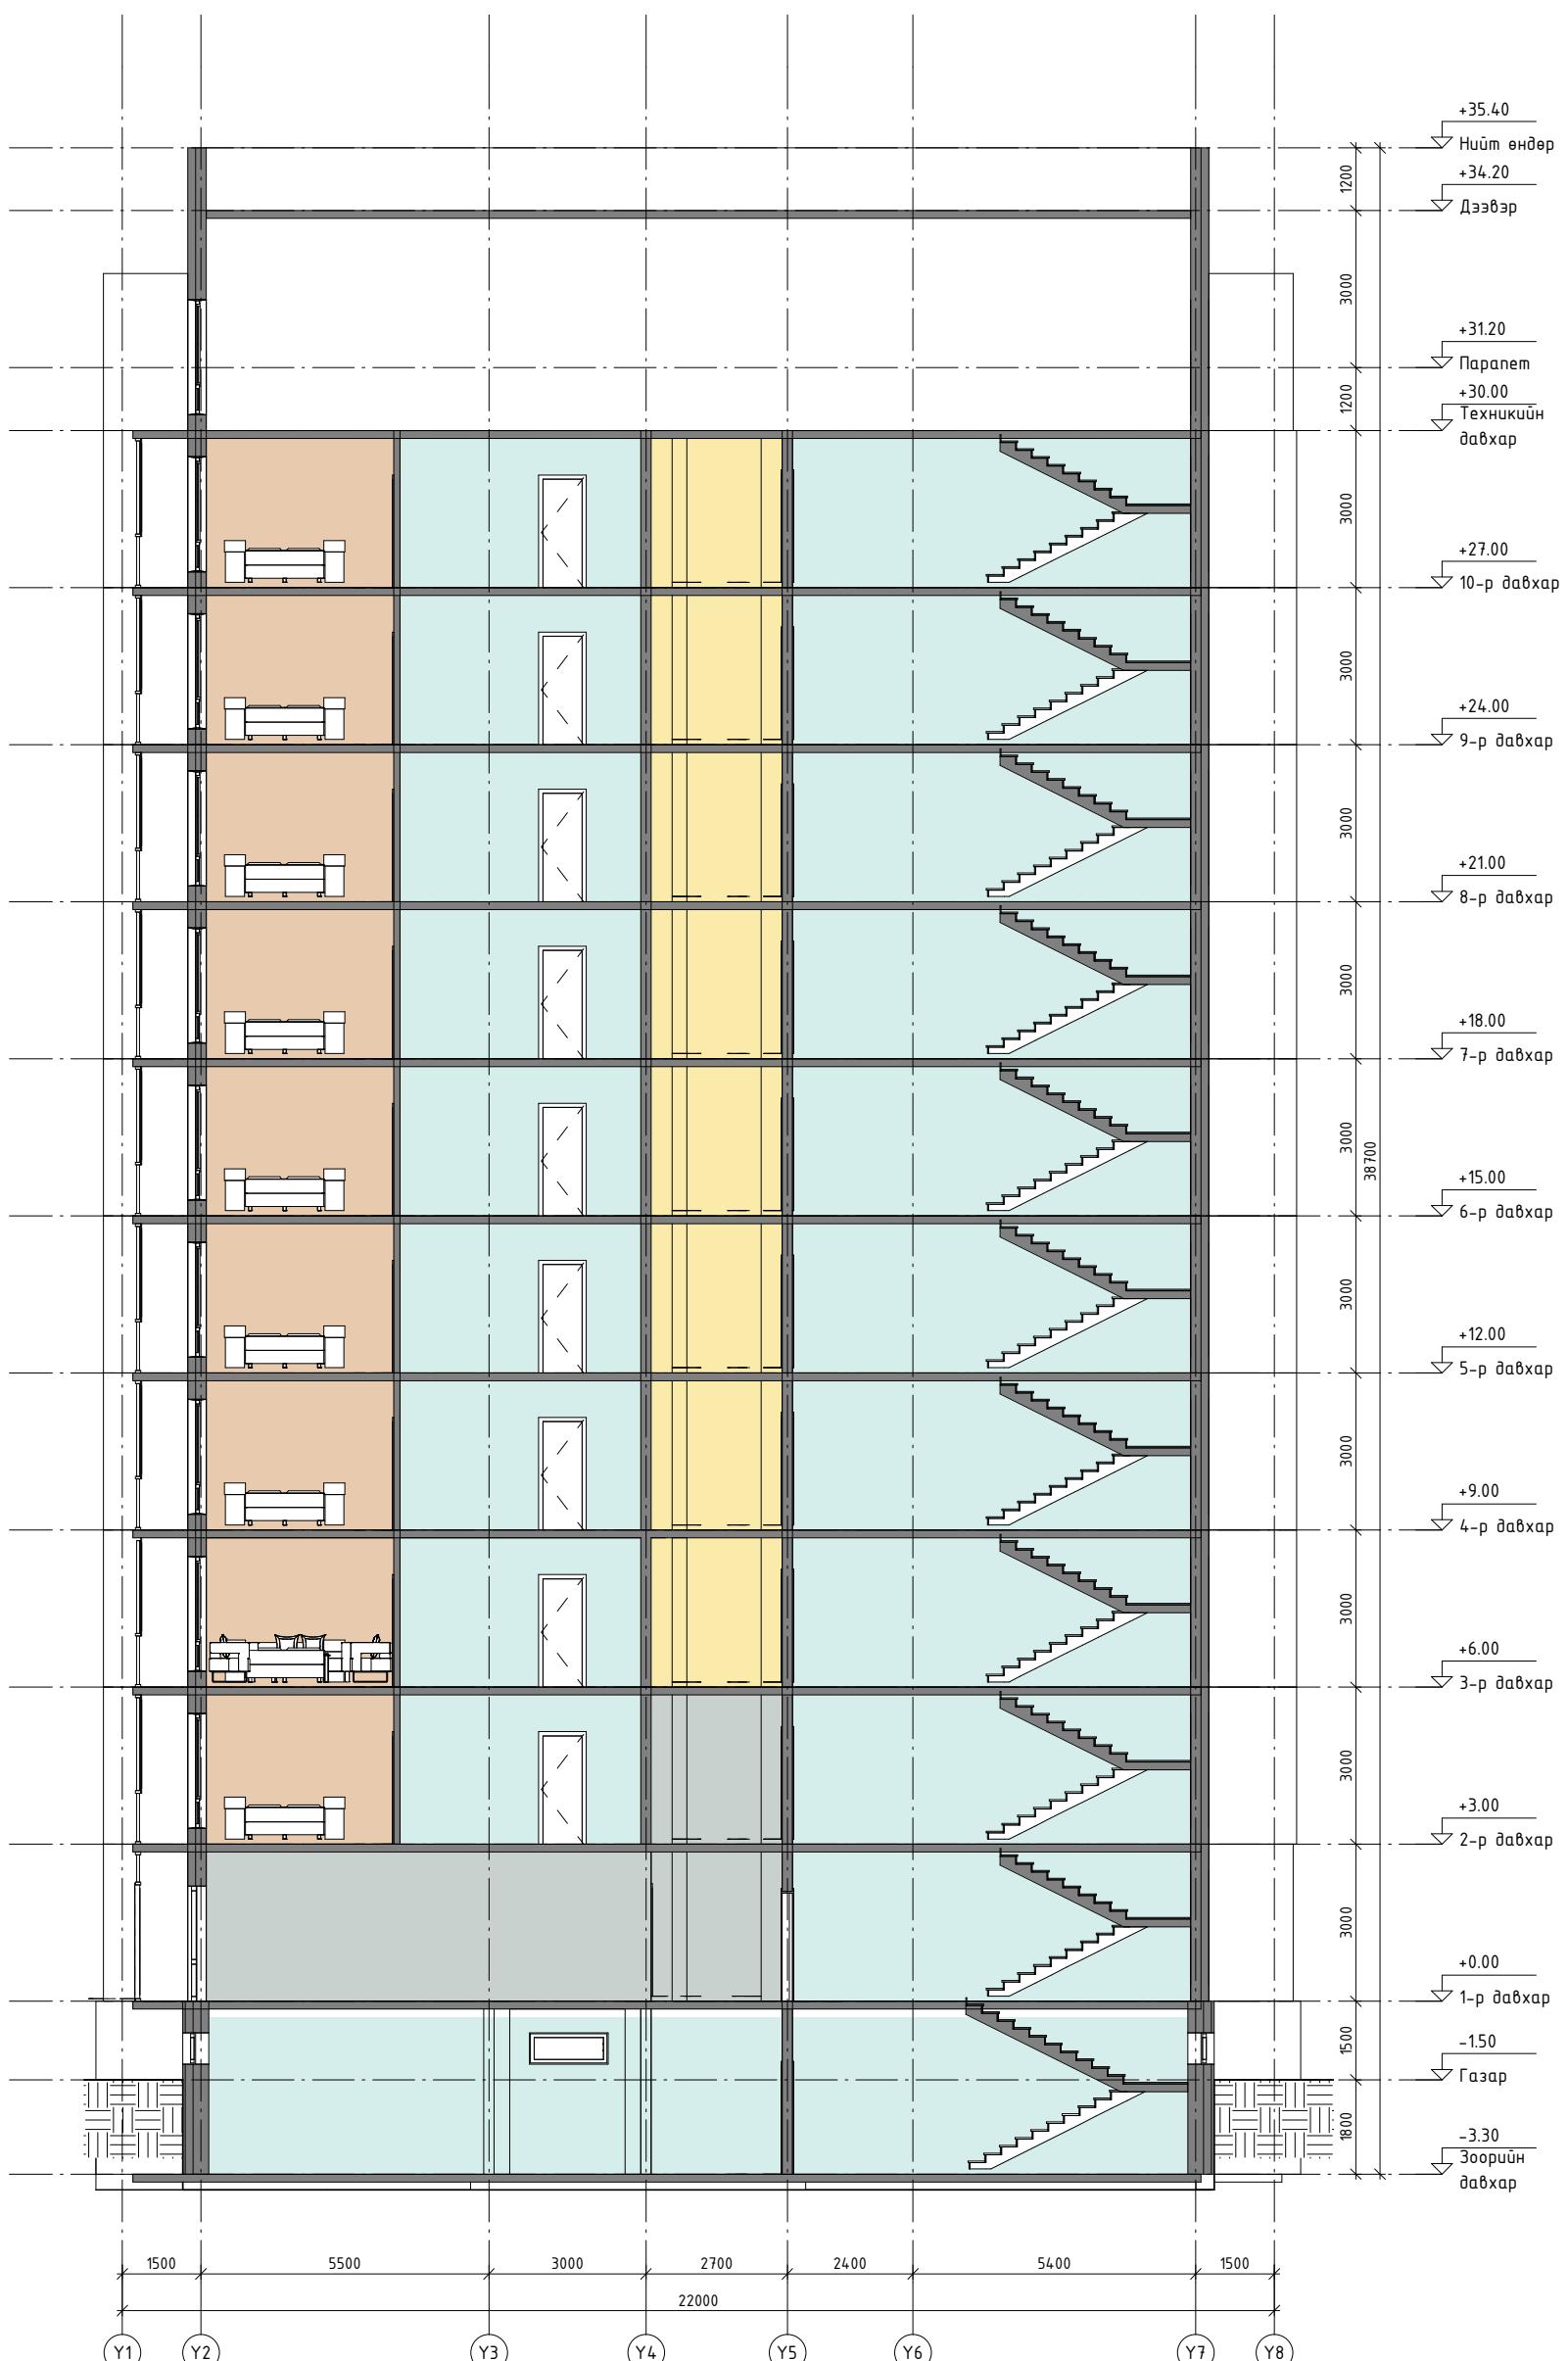

Чааандоатар хот, Сүхбаатар дүүрэг, 01-р хороо  
“ТАНЫ ТӨЛӨӨ БИД” ХХК-ИЙН 6 ДАВХАР ЭМНЭЛГИЙН БАРИЛГЫН ӨРГӨТГӨЛ

Огтпол-2


Үе шам: АЗ

Архитектор	Э.Анхбаяр	ЕГ шифр:	ПА-02/21	Масштаб:	1 : 100	Огноо:	9/9/2021 8:41:28 PM
Гүйцэтгэсэн	Г.Үүрцаан	ТГ шифр:	Эрсгүйн дүгээр:			Бүх дүгээр:	БА-47

Фасад 0 - а

М 1 : 100

1 : 100

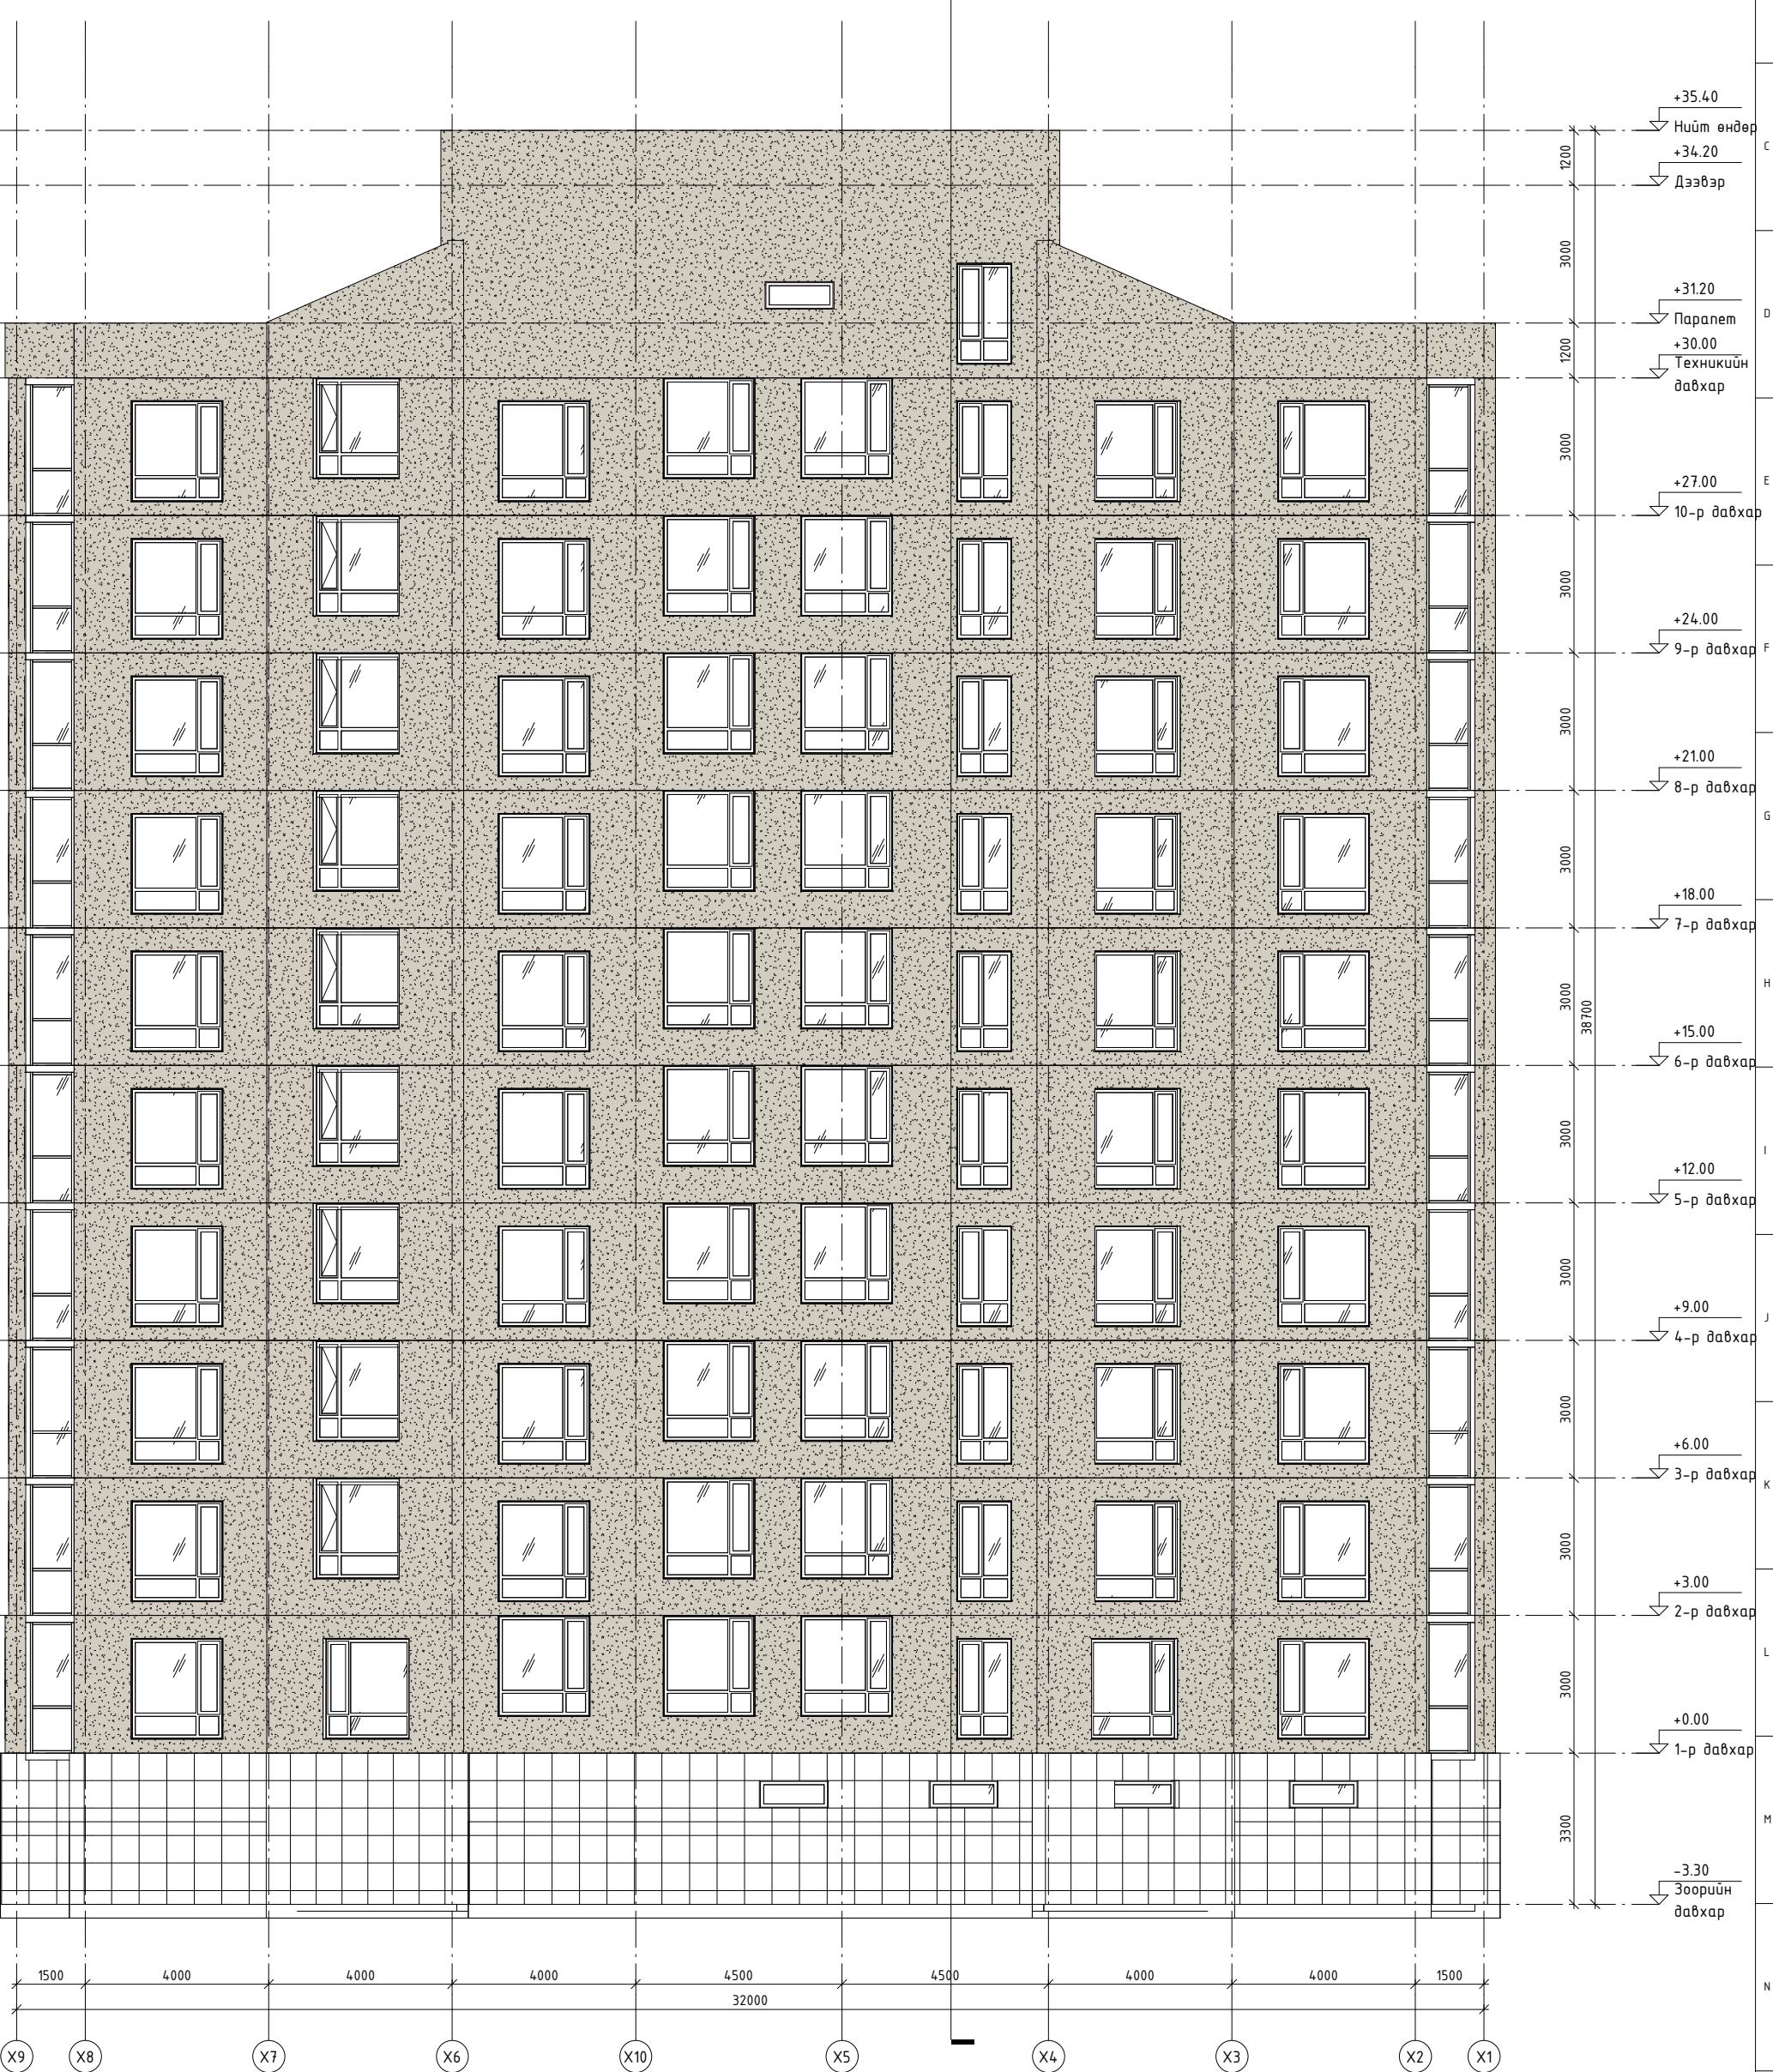1  
БА-12

Члаанбаатар хот, Сүхбаатар дүүрэг, 01-р хороо  
"ТАНЫ ТӨЛӨӨ БИД" ХХК-ИЙН 6 ДАВХАР ЭМНЭЛГИЙН БАРИЛГЫН ӨРГӨТГӨЛ

Нүүр тал А-В


Архитектор	Э.Анхбаяр	ЕГ шифр:	Масштаб:	Үе шам:
Гүйцэтгэсэн	Г.Үүрцаа	ПА-02/21	1 : 100	Огноо:
Шалгасан	Э. Анхбаяр	ИД-14/21	БА-14	9/9/2021 8:41:30 PM

Фасад 1 - а  
М 1 : 100


БА

Нүүр тал В-А, З-1

1 : 100

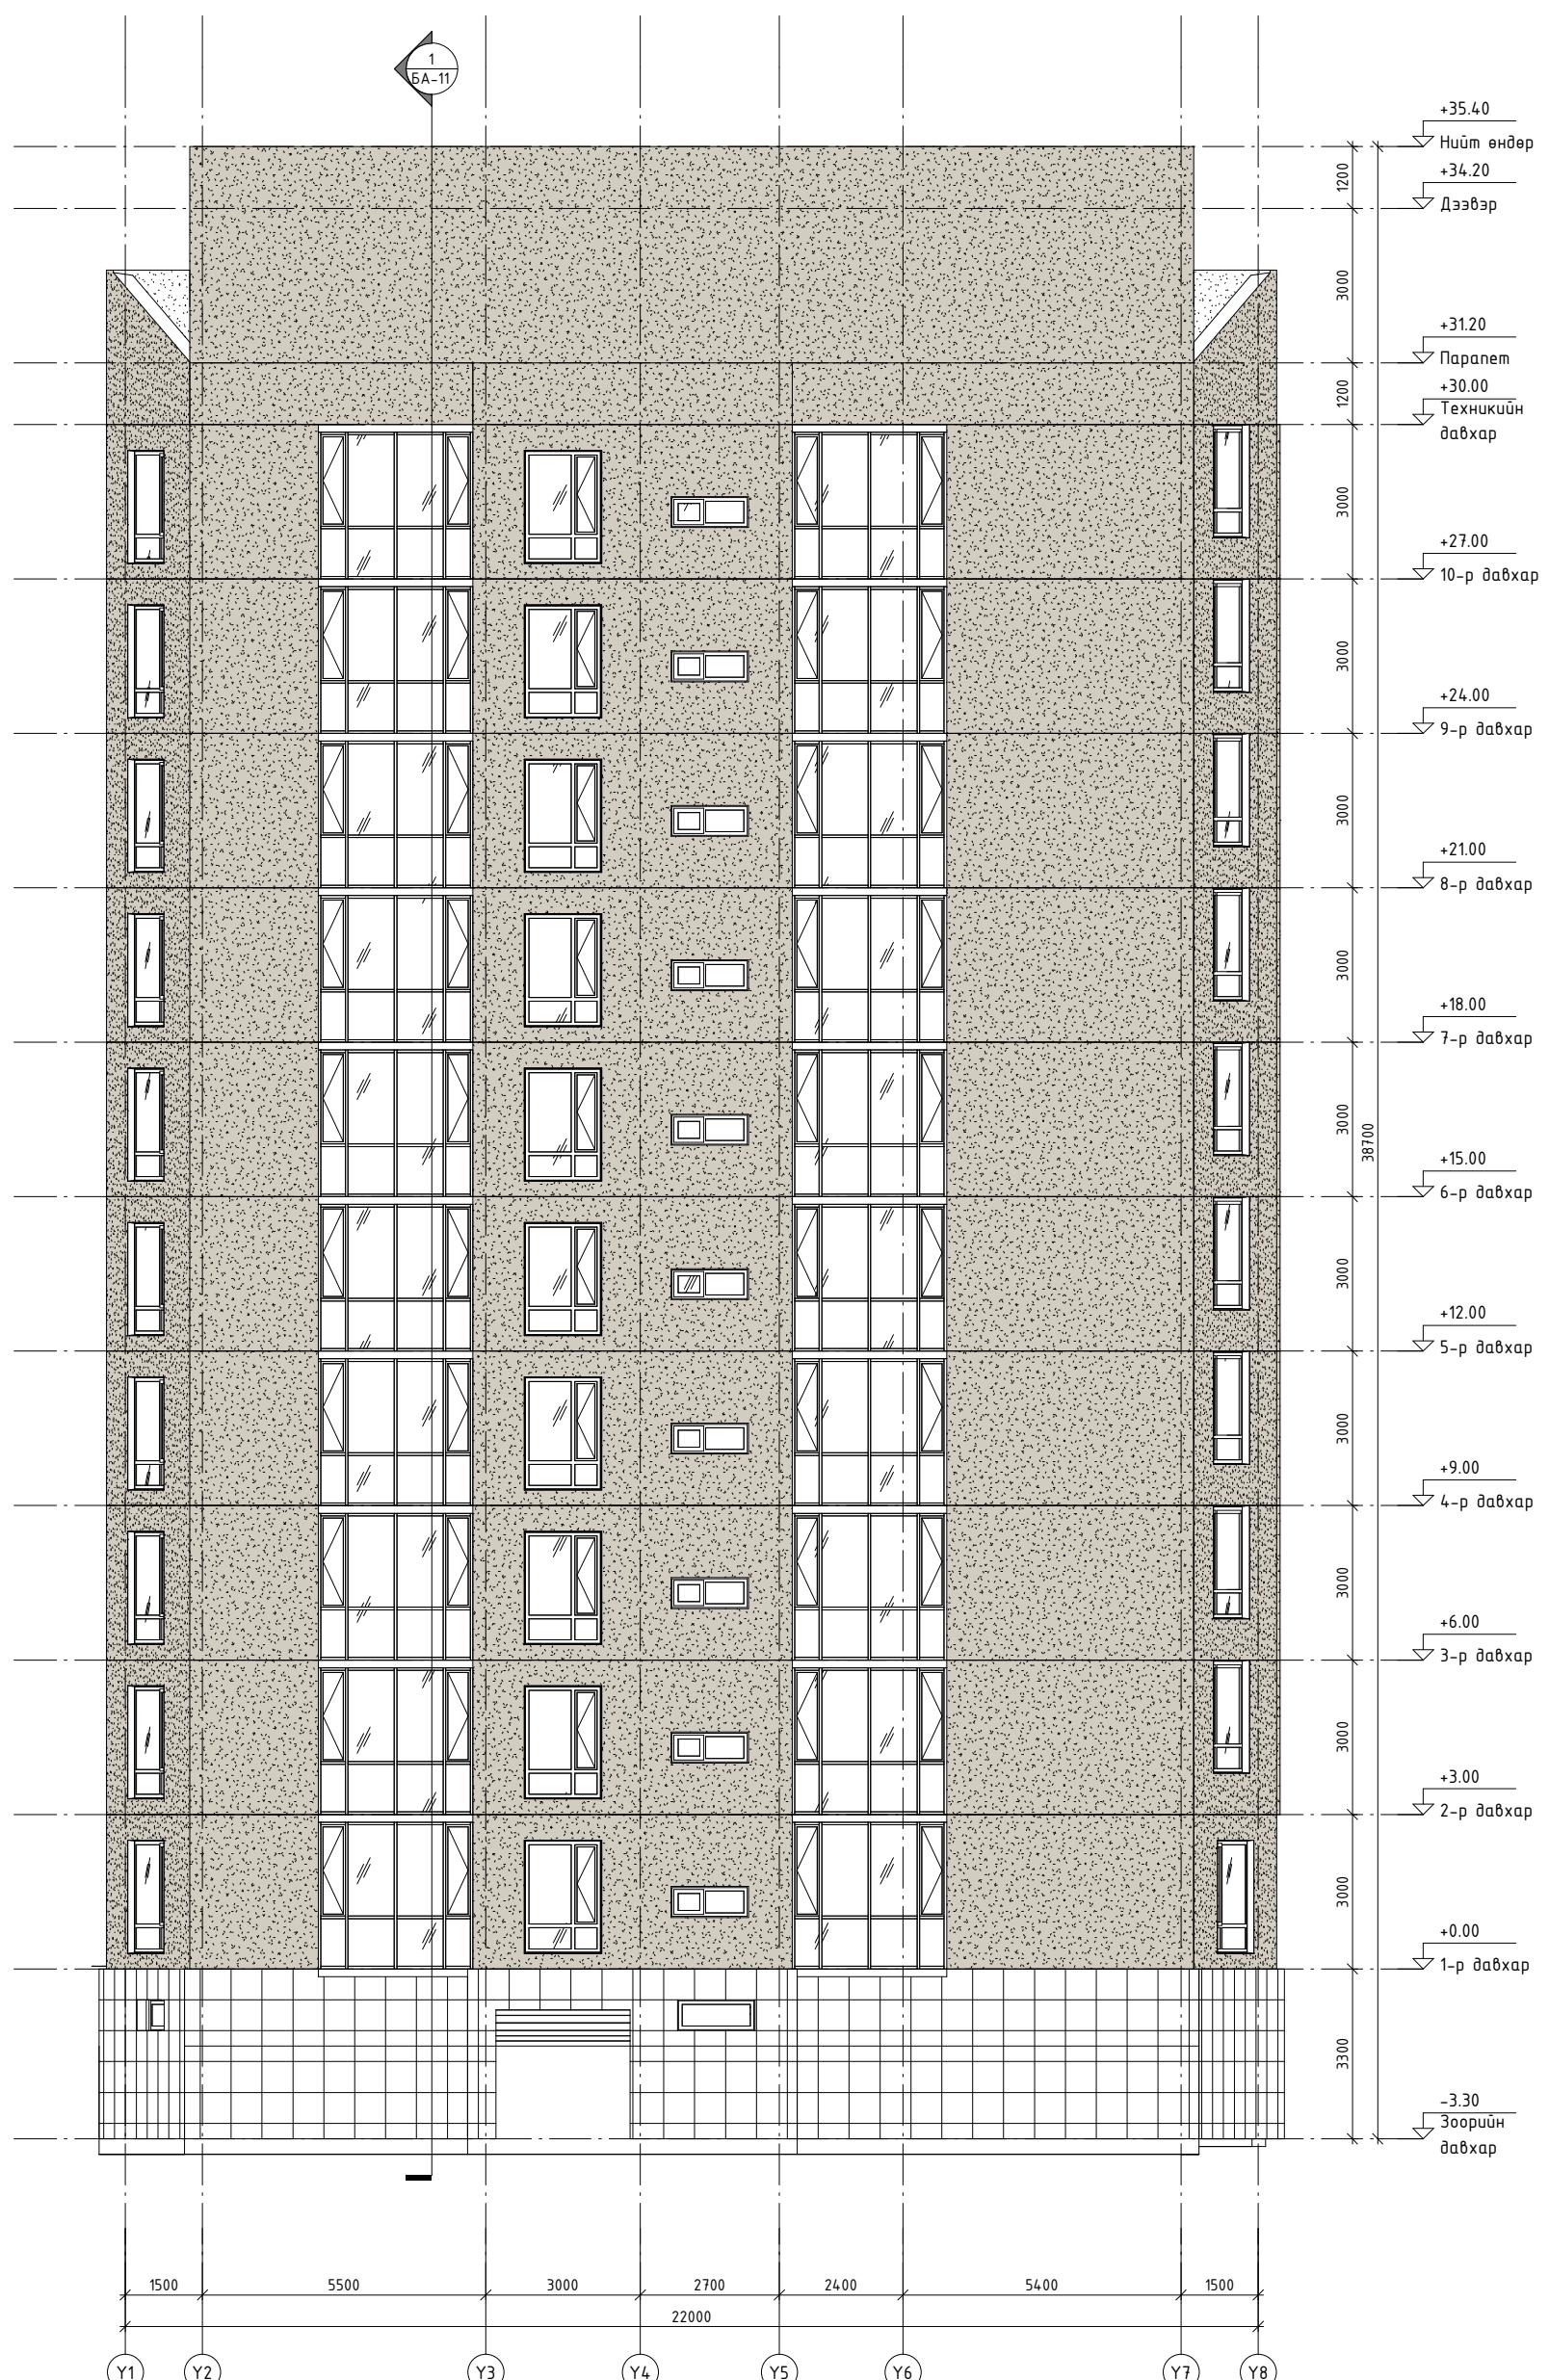

Чулаанбаатар хот, Сүхбаатар дүүрэг, 01-р хороо “ТАНЫ ТӨЛӨӨ БИД” ХХК-ИЙН 6 ДАВХАР ЭМНЭЛГИЙН БАРИЛГЫН ӨРГӨТГӨЛ				Үе шат:	A3
Нүүр тал В-А, З-1					
Архитектор		Э.Анхбаяр	ЕГ шифр:	ПА-02/21	Масштаб:
Гүйцэтгэсэн		Г.Үүрцааих	ТГ шифр:	Эзүргэн дүгээр	Огноо:
Шалгасан		Э. Аянхбаяр	ИД-14/21	БА-15	9/9/2021 8:41:31 PM

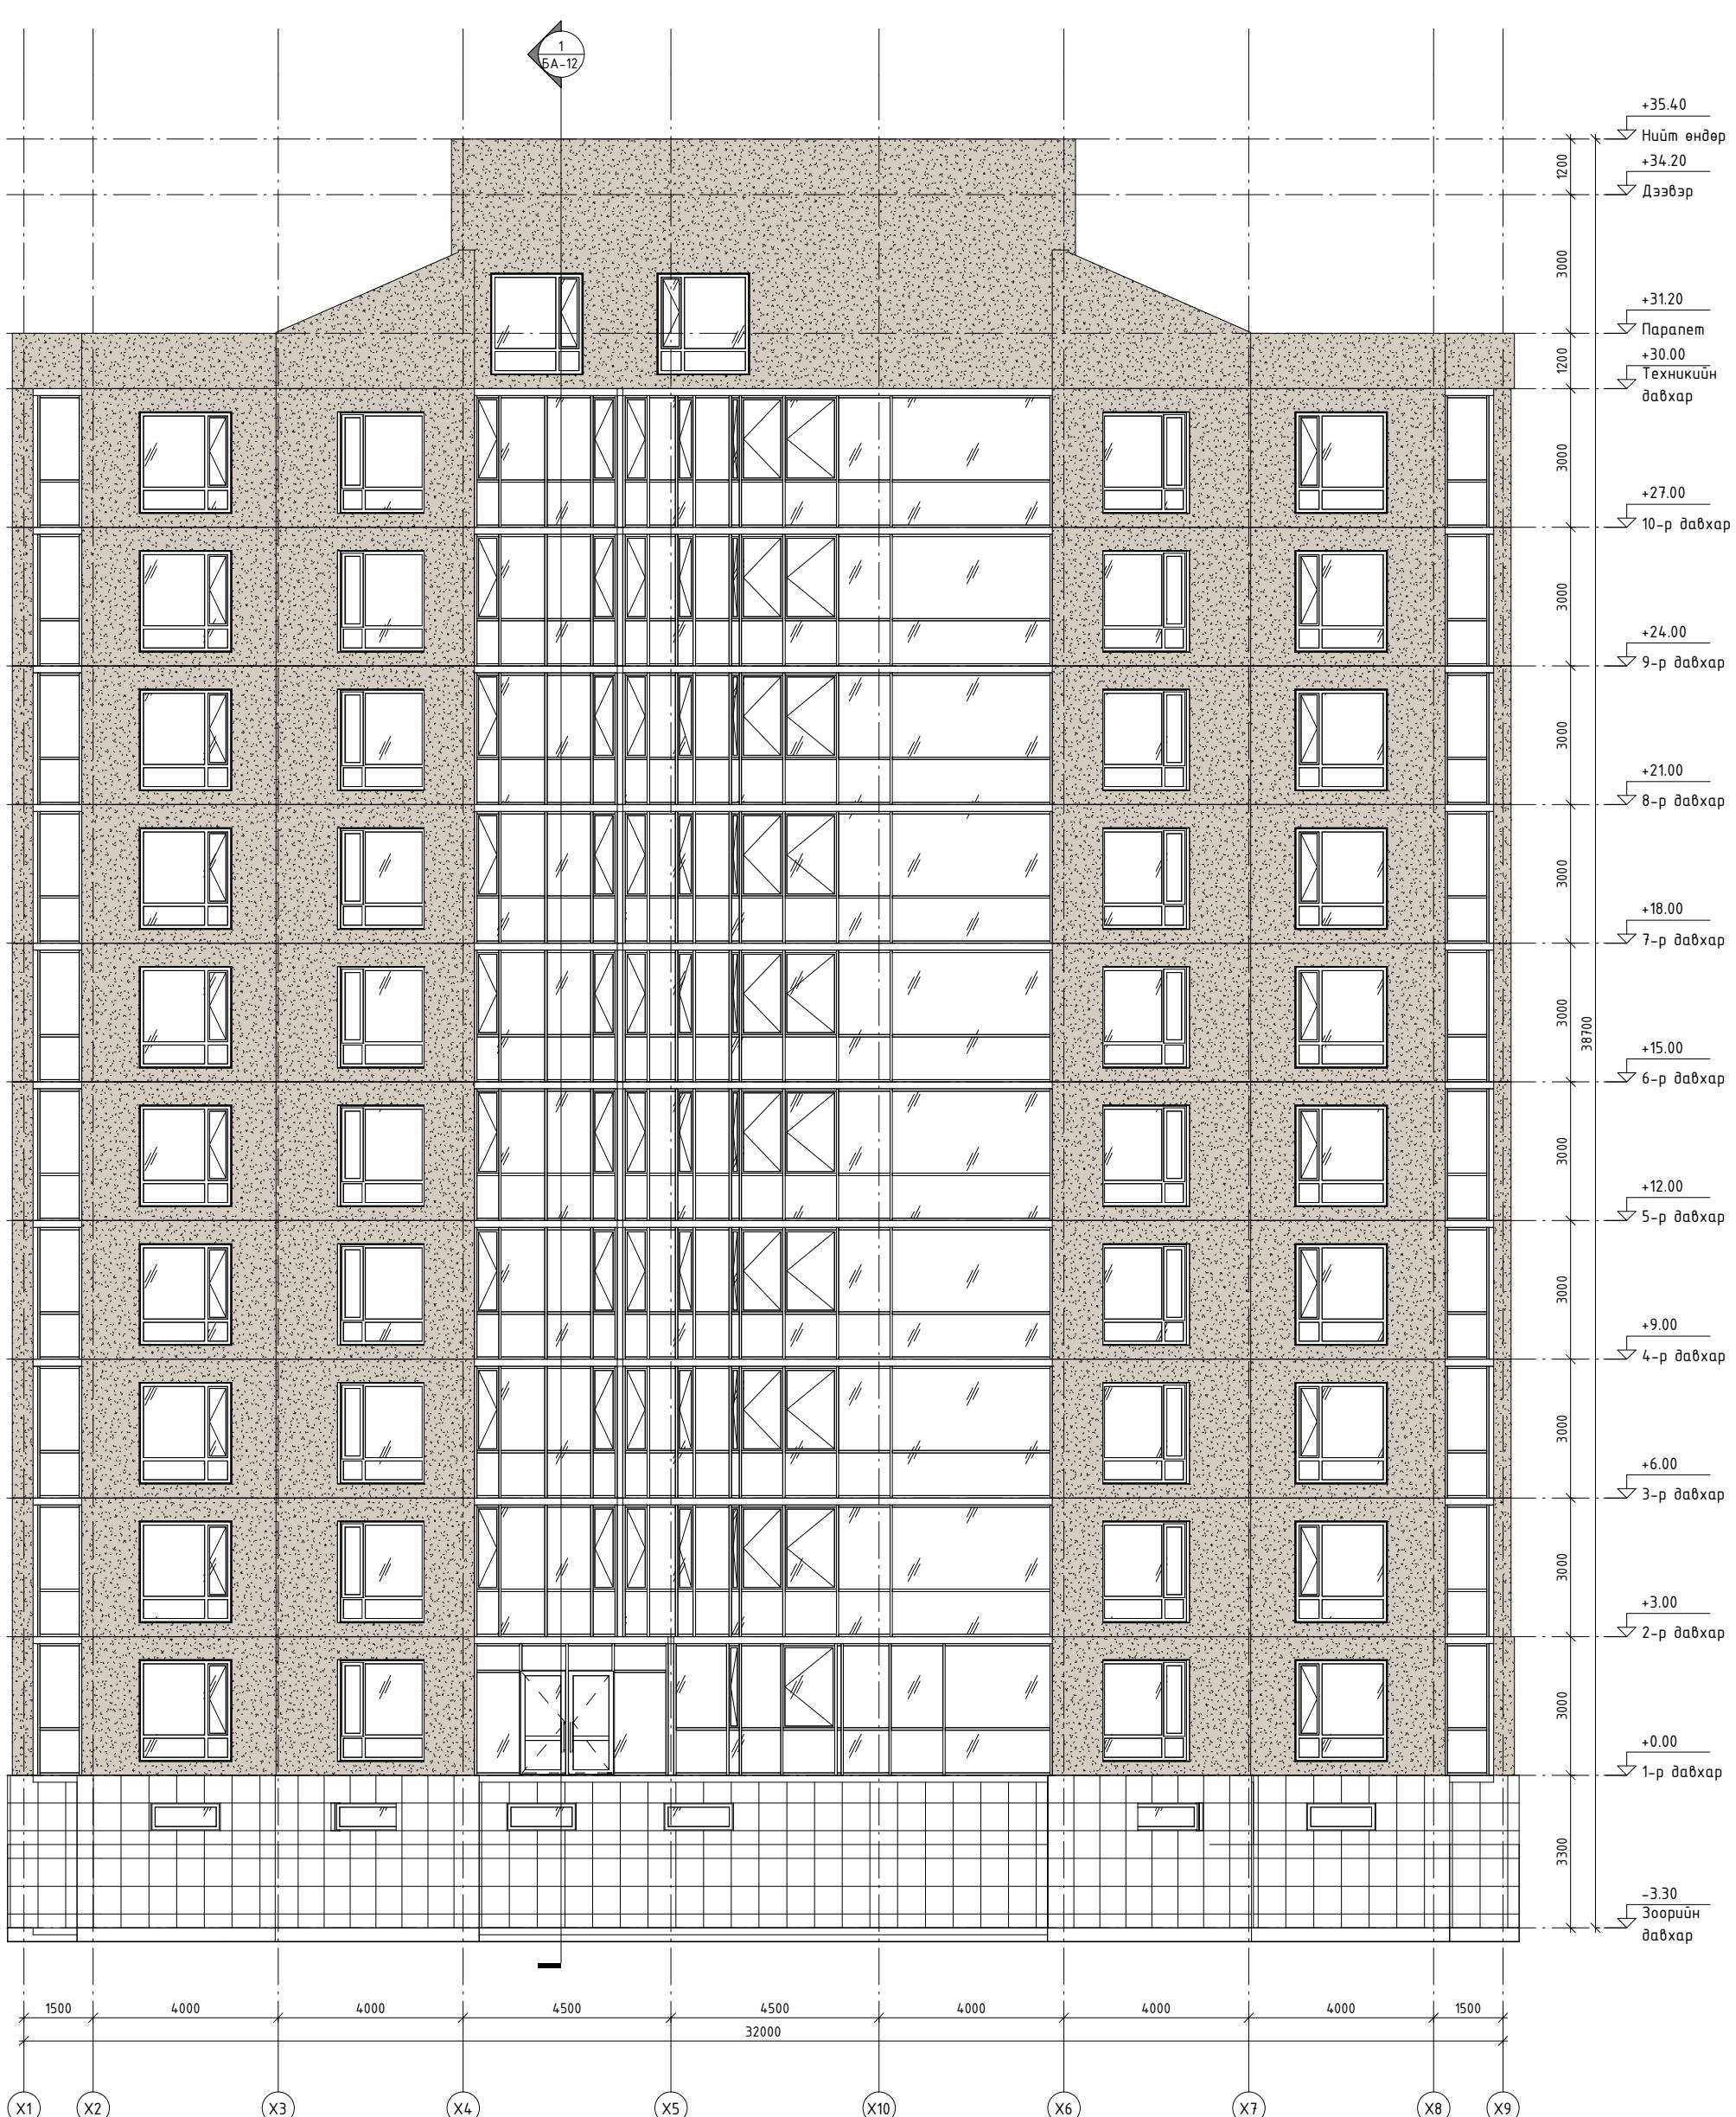

Члаанбаатар хот, Сүхбаатар дүүрэг, 01-р хороо

"ТАНЫ ТӨЛӨӨ БИД" ХХК-ИЙН 6 ДАВХАР ЭМНЭЛГИЙН БАРИЛГЫН ӨРГӨТГӨЛ

Нүүр тал 1-3

Үе шам: А3

Огноо: 9/9/2021 8:41:33 PM

Масштаб: 1 : 100


ТГ шифр: Энгийн дүгээр: Бүх дүгээр:

ПА-02/21 ИД-14/21 БА-16 БА-47

Э.Анхбаяр

Г.Үүрцаа

Шалгасан

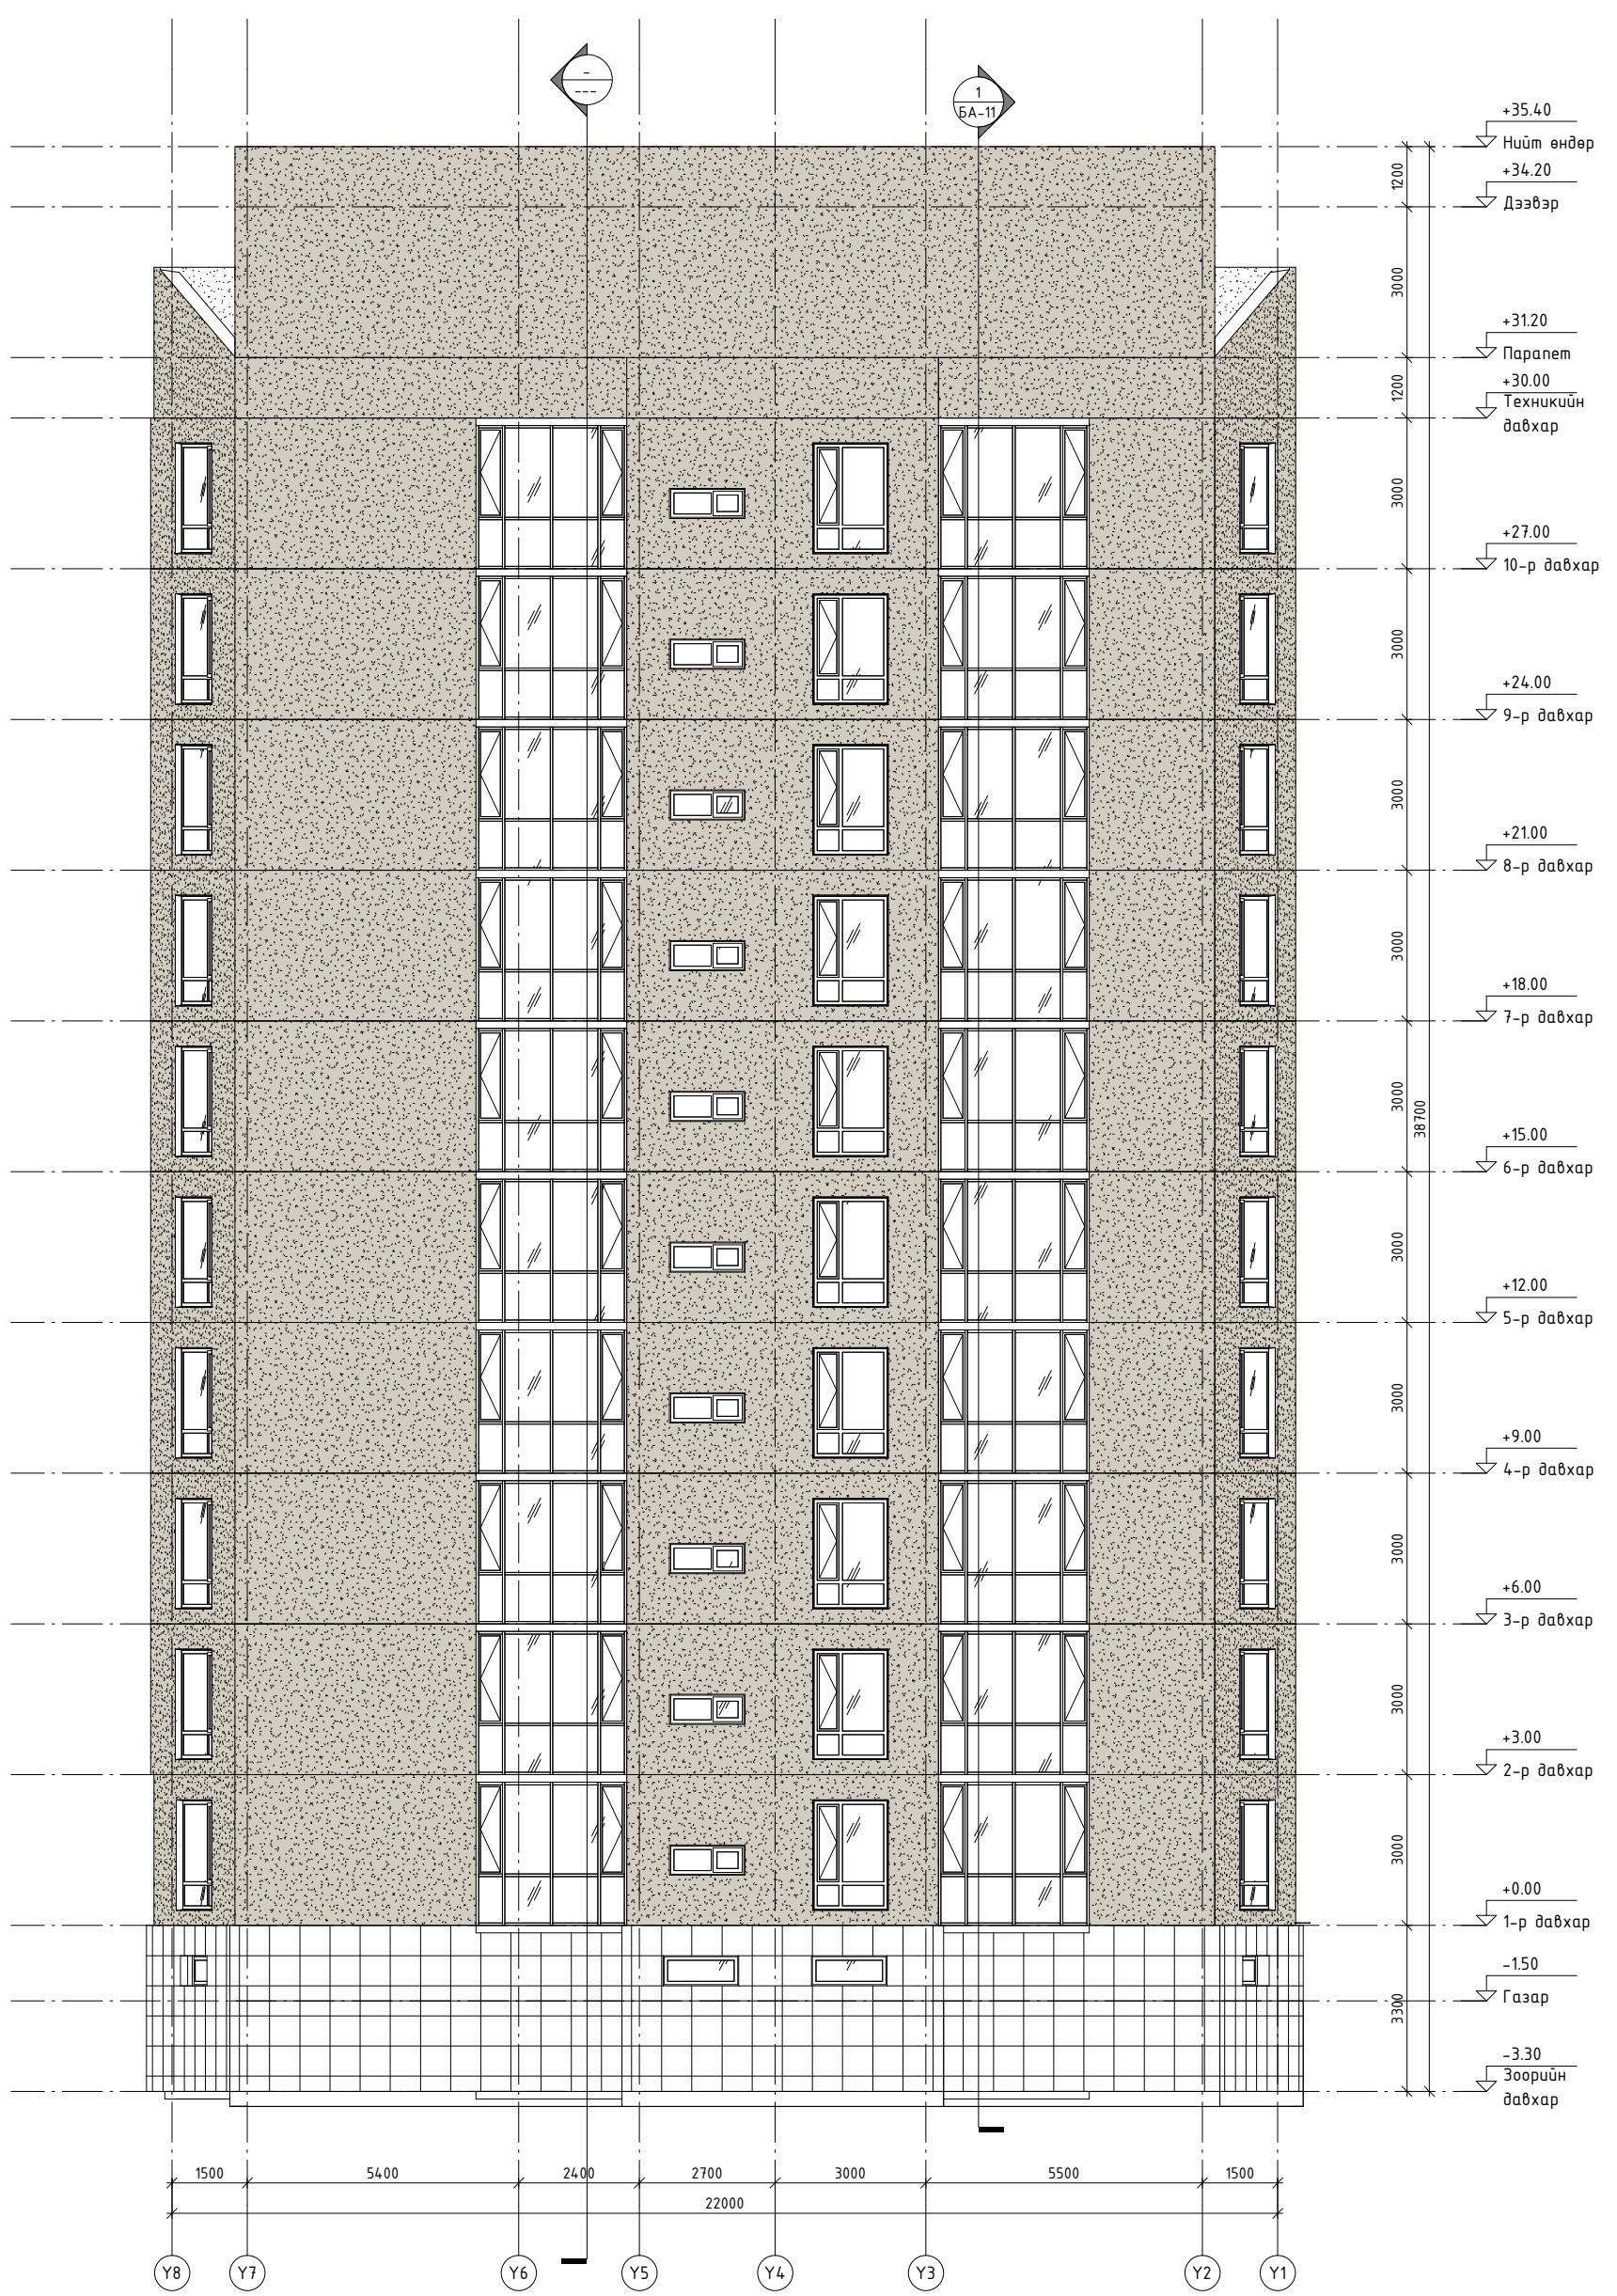

Фасад 3 - а

1 : 100



Чааандгаатар хом, Сүхбаатар дүүрэг, 01-р хороо

"ТАНЫ ТӨЛӨӨ БИД" ХХК-ИЙН 6 ДАВХАР ЭМНЭЛГИЙН БАРИЛГЫН ӨРГӨТГӨЛ

Нүүр тал -4

Ye шам:

A3

Designer

ЕГ шифр:

Масштаб:

Огноо:

1 : 100

9/9/2021 8:41:34 PM

Author

ТГ шифр:

Зүргийн дүгээр:

БА-17

Checker

Бүх дүгээр:



Члаанбаатар хот, Сүхбаатар дүүрэг, 01-р хороо  
“ТАНЫ ТӨЛӨӨ БИД” ХХК-ИЙН 6 ДАВХАР ЭМНЭЛГИЙН БАРИЛГЫН ӨРГӨТГӨЛ

1-р дэвхрын аксонометр дайгүүлэлт	Үе шам:	A3
-----------------------------------	---------	----

Архитектор	Э.Анхбаяр	ЕГ шифр:	ПА-02/21	Масштаб:	Огноо:
------------	-----------	----------	----------	----------	--------

Гүүцэмгэсэн	Г.Үүрцаах	ТГ шифр:	ИД-14/21	Зүргийн дүгээр:	Бүх дүгээр:
-------------	-----------	----------	----------	-----------------	-------------

Шалгасан	Э. Анхбаяр	БА-45	БА-47
----------	------------	-------	-------

A

B

C

D

E

F

G

H

A

B

C

D

E

F

G

H



